


| REV | DESCRIPTION                                | DATE       | BY |
|-----|--------------------------------------------|------------|----|
| P1  | Making sketch for the prototype build plan | 2026-10-02 | AC |

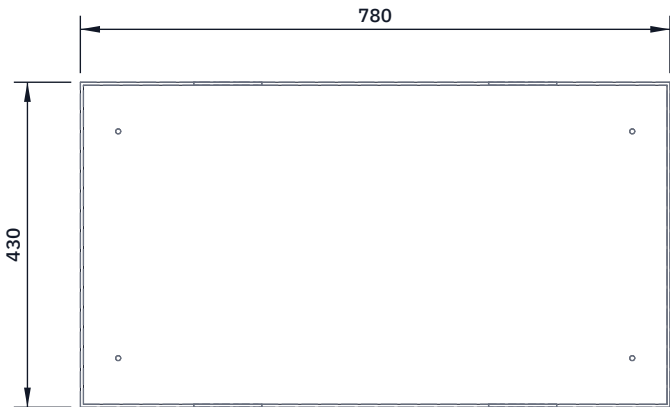


TOP VIEW  
Scale 1:10; looking down (along -Z)



FRONT VIEW  
Scale 1:10; looking at the front (along +Y)



RIGHT VIEW  
Scale 1:10; looking at the right side (along -X)

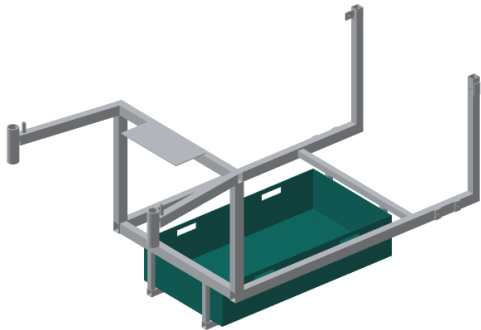

WHERE IT GOES  
This part in colour, its neighbours in grey

HOW TO MAKE IT AND HOW IT FITS

Floor 780 x 430, 6 mm. Side walls 2 x 780 x 160, end walls 2 x 422 x 160, 4 mm. Walls stand on the floor at its edges; the end walls fit between the side walls.

Hand holds: two 90 x 26 slots in each side wall, 17 below the top edge, centred 195 and 585 from the rear edge; round the ends.

Brackets outside: 10 along the bottom joints (3 per side, 2 per end), 4 up the corners; M4 bolts, washers both sides.

Four 6.6 mm holes in the floor for the bolts to the bearers, 150 each side of the centre line, 50 and 730 from the rear edge; countersink them from the inside so the pad lies flat.

Pad: 2 mm rubber, 772 x 422, laid loose on the floor.

Strap anchors: one M6 bolt with a large washer through each side wall, 20 up, at 186 and 594 from the rear edge.

Check: four jerrycans drop in 2 x 2 with 2 mm to the walls.

|                                                                                         |             |   |                                          |                 |                       |
|-----------------------------------------------------------------------------------------|-------------|---|------------------------------------------|-----------------|-----------------------|
| WATERWALKER                                                                             |             |   | github.com/BoujeeEnjinia1701/waterwalker |                 |                       |
| WaterWalker cradle (floor and walls): making sketch                                     |             |   |                                          |                 |                       |
| DRAWING NO.<br>WWK-DWG-108                                                              |             |   | REV<br>P1                                | SHEET<br>1 of 1 | SIZE<br>ANSI B        |
| SCALE<br>1:10                                                                           | UNITS<br>mm | PROJECTION<br> | DATE<br>2026-10-02                       |                 | DRAWN<br>Amish Chadha |
| MATERIAL / NOTES<br>Exterior plywood 6 mm (floor) and 4 mm (walls); zinc angle brackets |             |   |                                          |                 |                       |
| Licensed CERN-OHL-S-2.0 · Design Molecule Lab · designmolecule.com                      |             |   |                                          |                 |                       |
| Generated from cad/src; do not edit by hand                                             |             |   |                                          |                 |                       |